


CÔNG TY CỔ PHẦN THỦY ĐIỆN VĨNH SƠN - SÔNG HÌNH
NHÀ MÁY THỦY ĐIỆN VĨNH SƠN


NÂNG CẤP HỆ THỐNG UPS CẤP NGUỒN 220VAC
 - NHÀ MÁY THỦY ĐIỆN VĨNH SƠN

	Chức vụ	Họ và tên	Chữ ký	Ngày	CÔNG TY CỔ PHẦN THỦY ĐIỆN VĨNH SƠN - SÔNG HÌNH NHÀ MÁY THỦY ĐIỆN VĨNH SƠN	HỆ THỐNG MÁY PHÁT DIESEL 20LKP - NHÀ MÁY VĨNH SƠN
Duyệt	P.TGD	Dương Tấn Tường				SƠ ĐỒ ĐIỆN
Kiểm tra	T.PKT	Hồ Đắc Toàn				Tên bản vẽ: VIN20-UPS-2025
Vẽ	Trực chính	Trương Văn Đông				

SƠ ĐỒ CẤP NGUỒN 220VAC CHO CÁC BỘ UPS

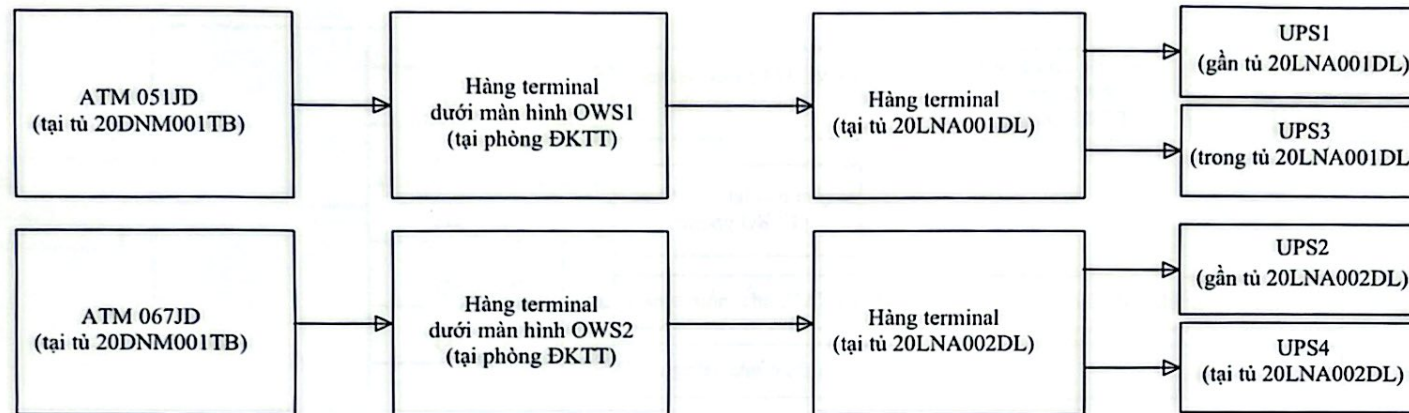

SƠ ĐỒ ĐẦU NỐI CỦA BỘ UPS VÀ ACQUY MỚI

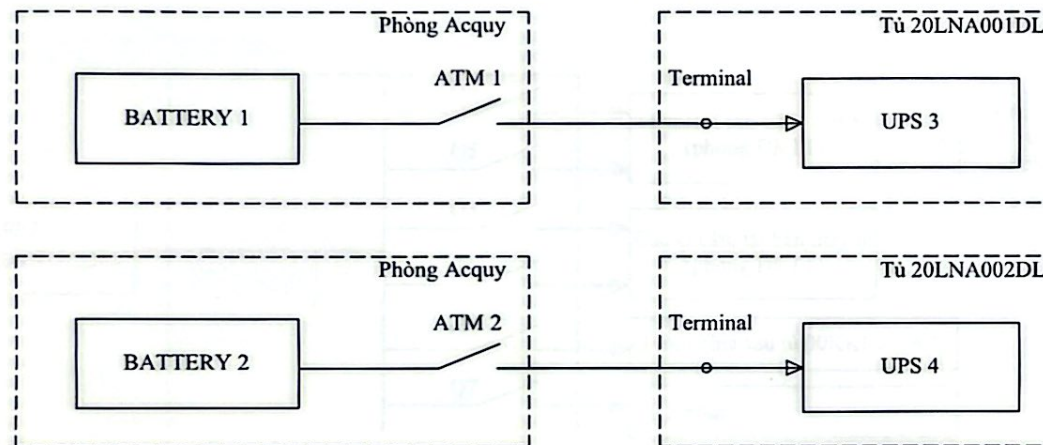

Chú thích:


- + UPS1, UPS2: là hai bộ UPS cũ, tích hợp Acquy bên trong. Được chuyển xuống đặt tại phòng Một chiều.
- + UPS3, UPS4: là hai bộ Inverter mới, có Acquy lắp riêng bên ngoài. Được lắp đặt trong hai tủ 20LNA001DL, 20LNA002DL.
- + Battery1, Battery2: là hai dàn Acquy rời của hai bộ UPS3 và UPS4. Đặt tại phòng Acquy.
- + Tủ 20LNA001DL, 20LNA002DL: là hai tủ nghịch lưu cũ, đặt tại phòng Một chiều.

SƠ ĐỒ TỔNG QUAN





Trang

1

SƠ ĐỒ CHI TIẾT CẤP NGUỒN CHO PHỤ TẢI CỦA CÁC BỘ UPS 1 VÀ UPS 2

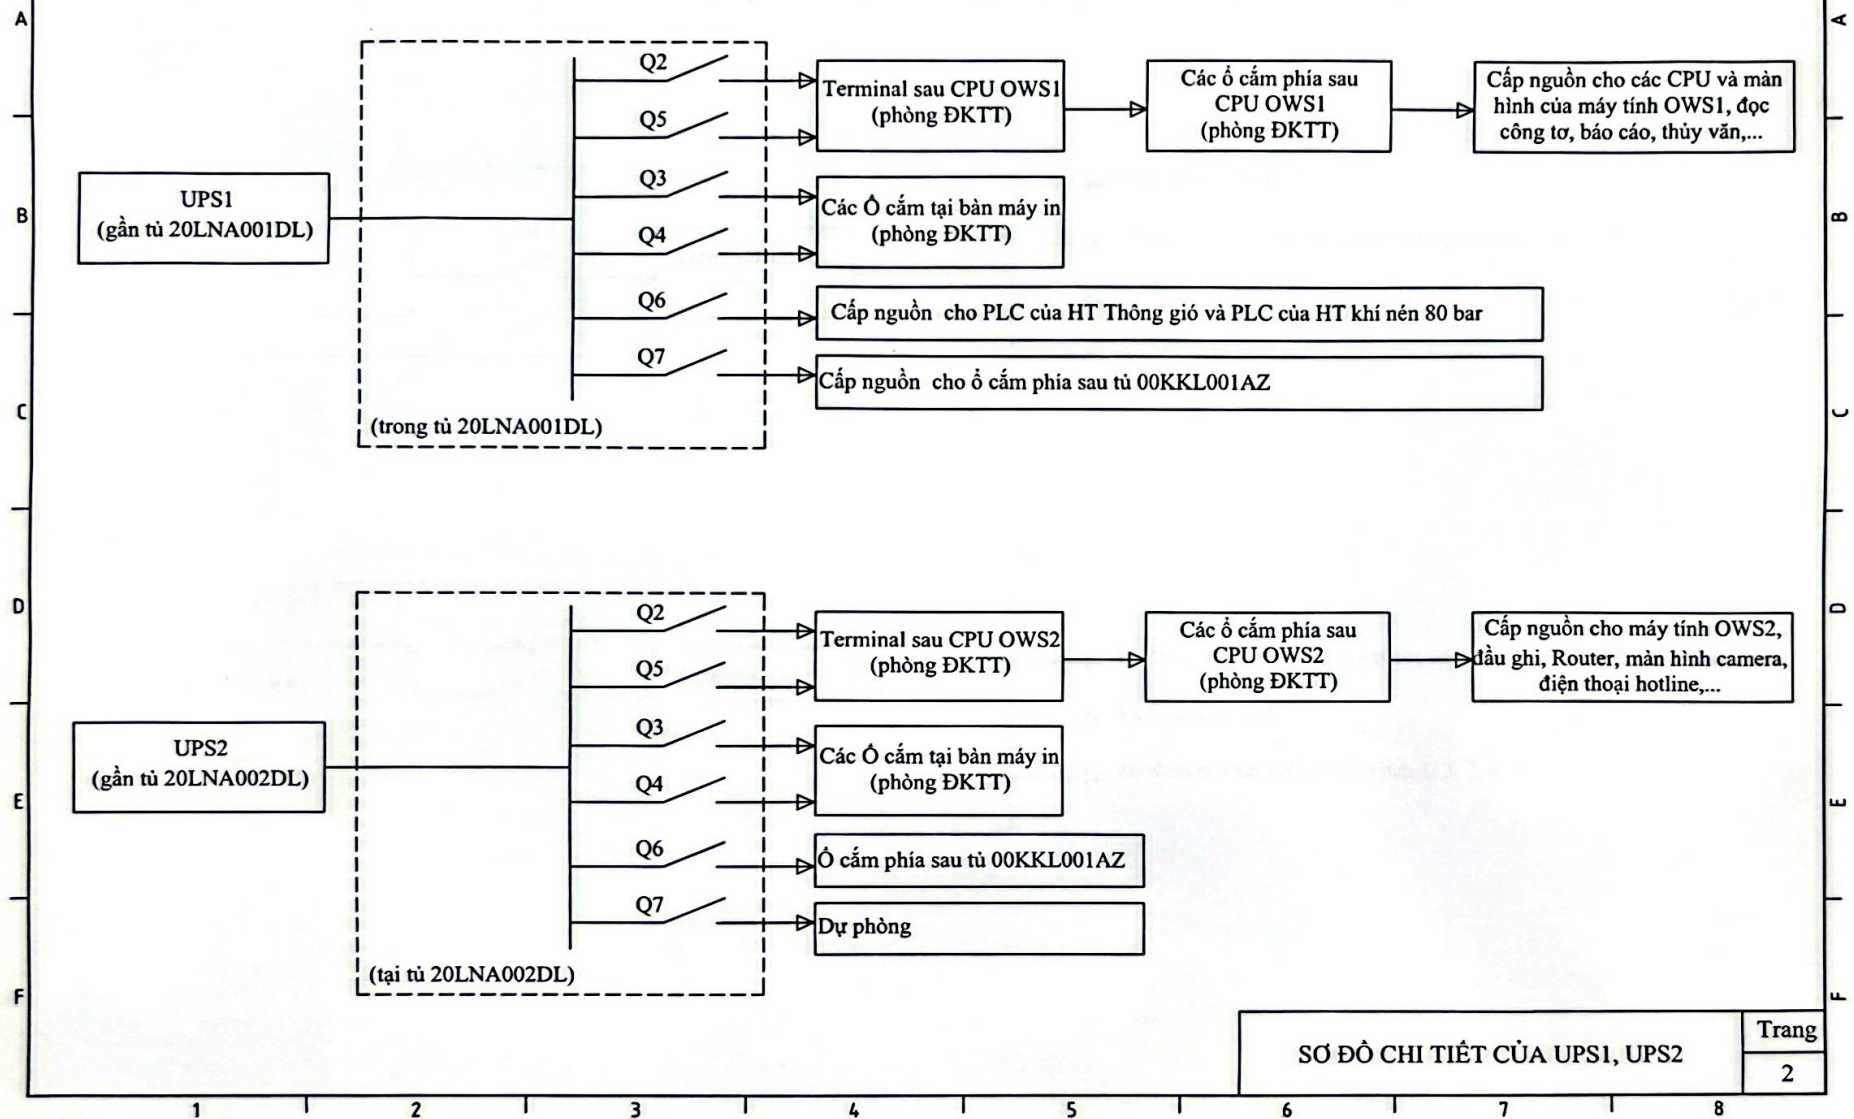

SƠ ĐỒ CHI TIẾT CẤP NGUỒN CHO PHỤ TẢI CỦA CÁC BỘ UPS 3, UPS 4

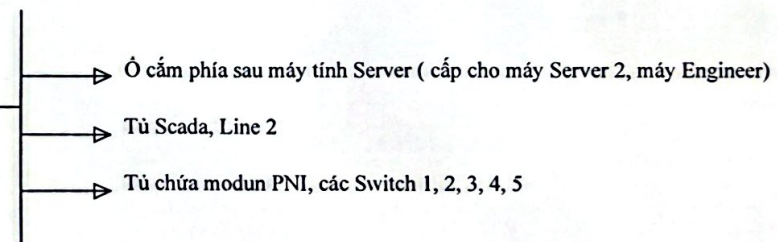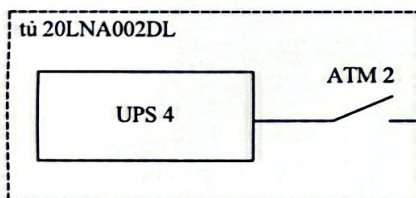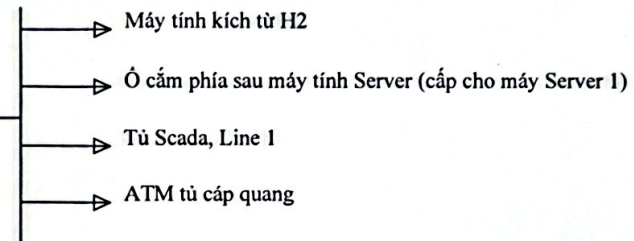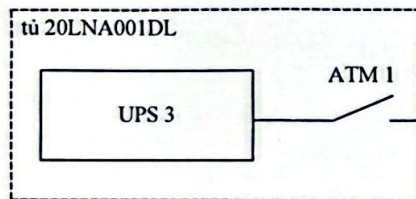

SƠ ĐỒ CHI TIẾT CỦA UPS 3, UPS 4

Trang
3