


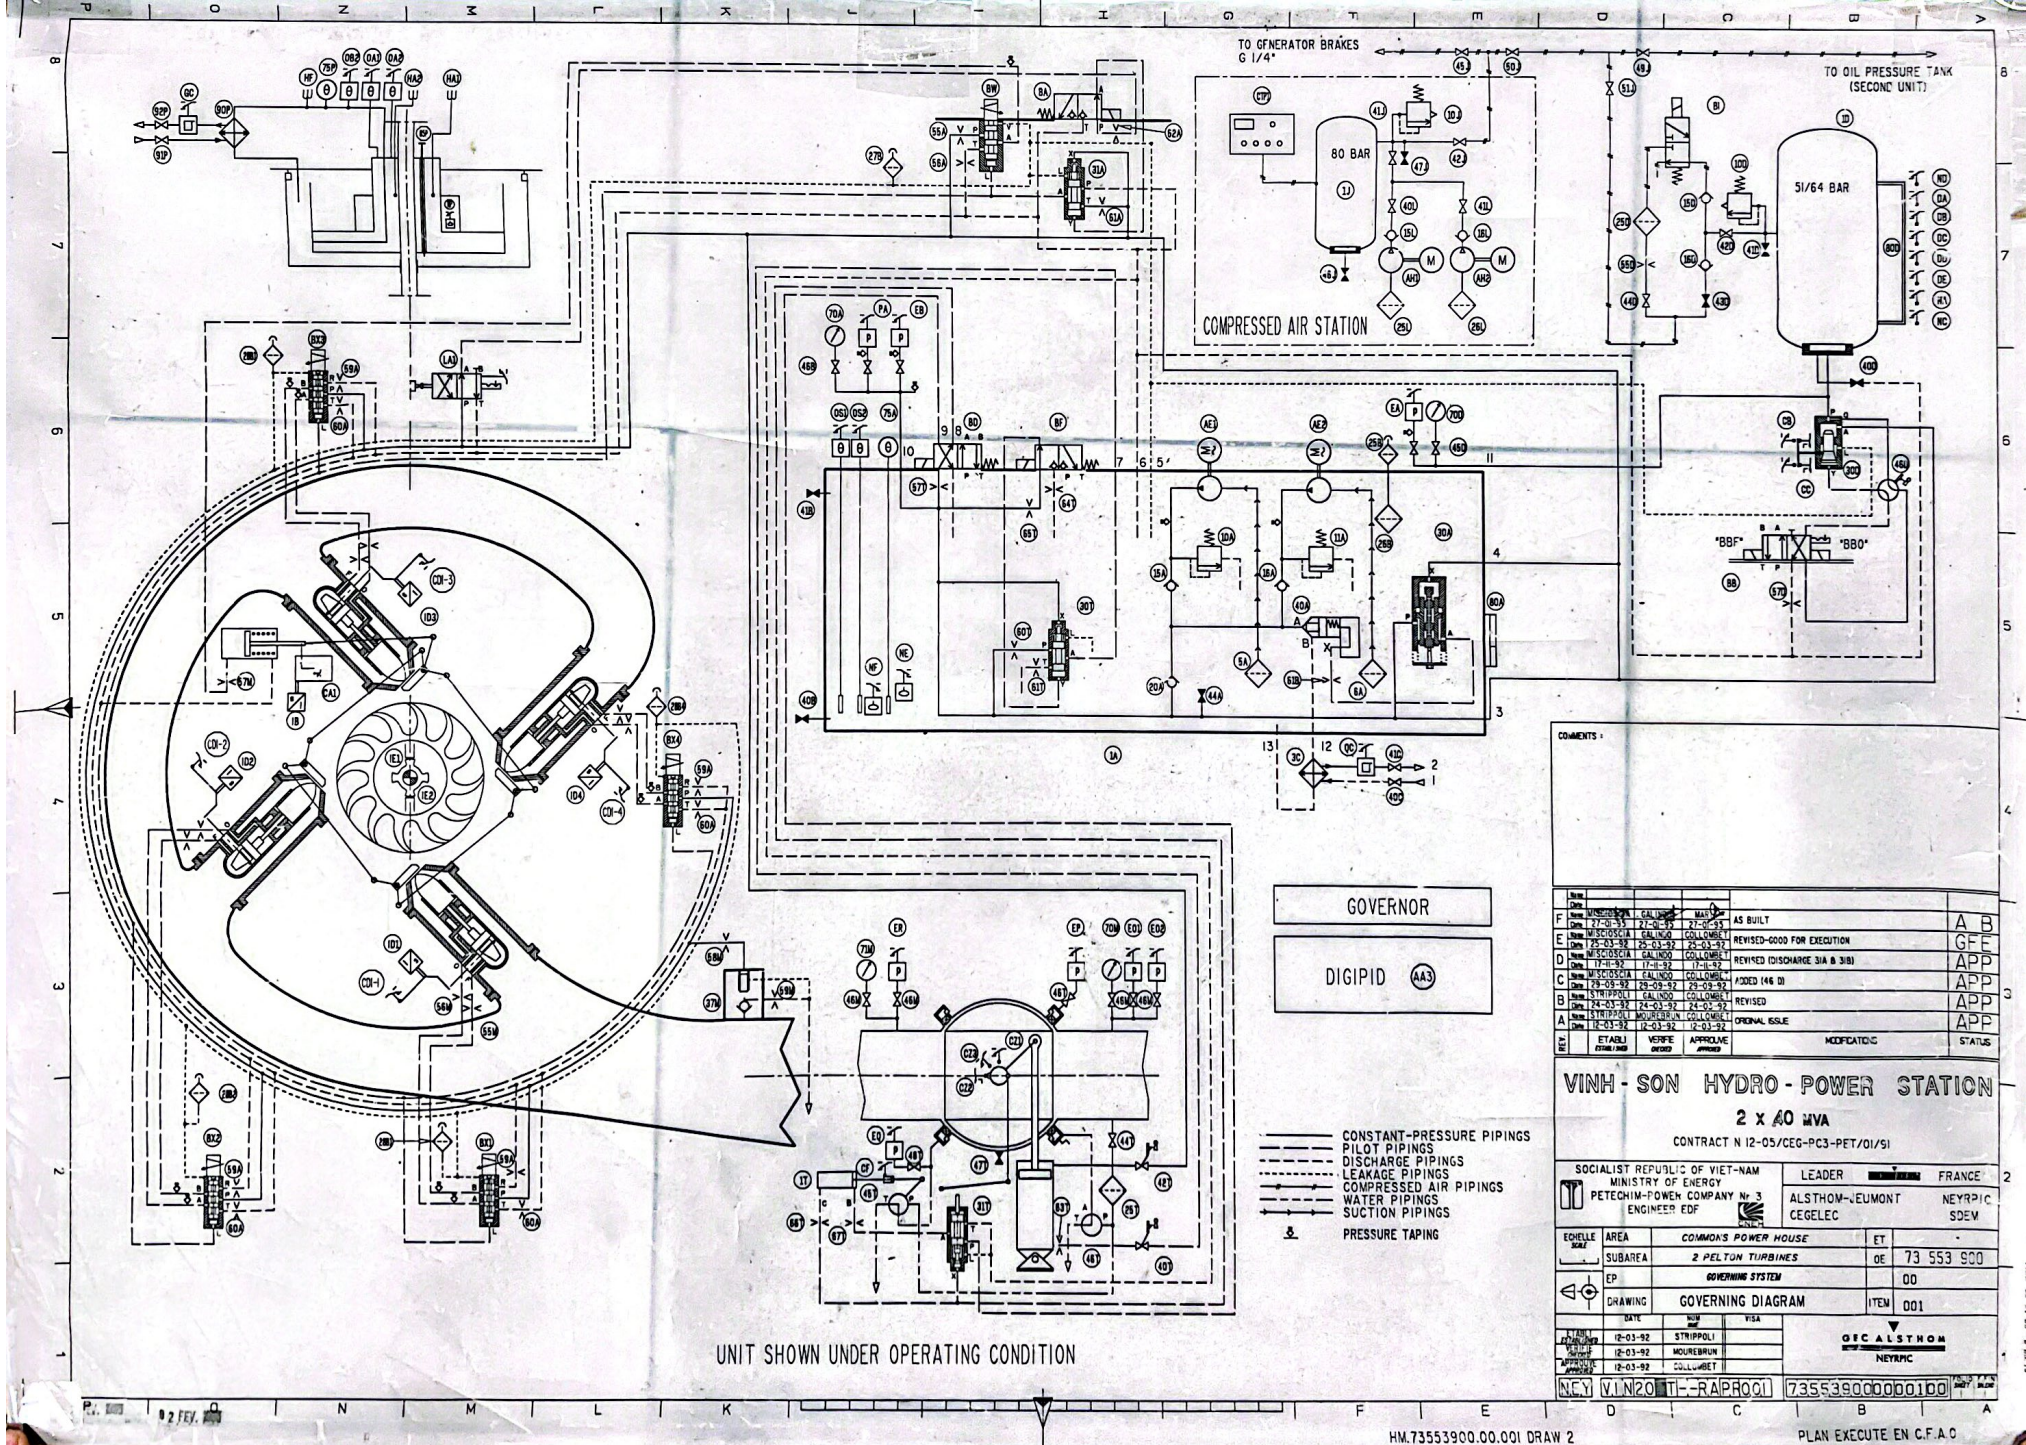

COMMENTS :

REV.	ETABL.	VERIF.	APPROUVE	MODIFIC.	STATUS
F	27-03-92	27-03-92	27-03-92	AS BUILT	A B
E	25-03-92	25-03-92	25-03-92	REVISED-GOOD FOR EXECUTION	GFE
D	25-03-92	25-03-92	25-03-92	REVISED (DISCHARGE 3/A B 3/B)	APP
C	27-03-92	27-03-92	27-03-92	ADDED (146 DI)	APP
B	24-03-92	24-03-92	24-03-92	REVISED	APP
A	12-03-92	12-03-92	12-03-92	ORIGINAL ISSUE	APP

VINH-SON HYDRO-POWER STATION
2 x 40 MVA

CONTRACT N 12-05/CEG-PC3-PET/01/91

SOCIALIST REPUBLIC OF VIET-NAM		LEADER		FRANCE	
MINISTRY OF ENERGY		ALSTHOM-UEMONT		NEYPIC	
PETECHIM-POWER COMPANY N° 3		CEGELEC		SDEW	
ENGINEER EDF					

ECHELLE	AREA	COMMON'S POWER HOUSE	ET
1/1	SUBAREA	2 PELTON TURBINES	DE 73 553 900
EP		GOVERNING SYSTEM	00
DRAWING		GOVERNING DIAGRAM	ITEM 001

DATE	BY	VISA
12-03-92	STRIPPOLI	
12-03-92	MOURMUR	
12-03-92	CULLIQUET	

ALSTHOM
NEYPIC

VCY VIN2011-RAPROOI 735539000000100

HM.73553900.00.001 DRAW 2

PLAN EXECUTE EN C.F.A.C